Nr	Y	X	H	Kodi	Përshkrimi	Burimi
2	7508341.840	4696777.923	606.713	40	Shtëpi-Ndërtesë	PM
6	7508337.302	4696773.278	606.713	40	Shtëpi-Ndërtesë	PM
17	7508329.215	4696780.387	606.713	40	Shtëpi-Ndërtesë	PM
20	7508328.464	4696776.214	606.713	40	Shtëpi-Ndërtesë	PM
21	7508327.580	4696776.373	606.713	40	Shtëpi-Ndërtesë	PM
24	7508327.112	4696773.824	606.713	40	Shtëpi-Ndërtesë	PM
25	7508327.996	4696773.674	606.713	40	Shtëpi-Ndërtesë	PM
35	7508340.865	4696772.544	606.713	40	Shtëpi-Ndërtesë	PM
37	7508336.678	4696769.938	606.713	40	Shtëpi-Ndërtesë	PM
38	7508336.362	4696769.982	606.713	40	Shtëpi-Ndërtesë	PM
39	7508334.951	4696769.015	606.713	40	Shtëpi-Ndërtesë	PM
40	7508333.108	4696769.414	606.713	40	Shtëpi-Ndërtesë	PM
41	7508332.215	4696770.638	606.713	40	Shtëpi-Ndërtesë	PM
43	7508331.794	4696770.895	606.713	40	Shtëpi-Ndërtesë	PM
44	7508327.626	4696771.688	606.713	40	Shtëpi-Ndërtesë	PM

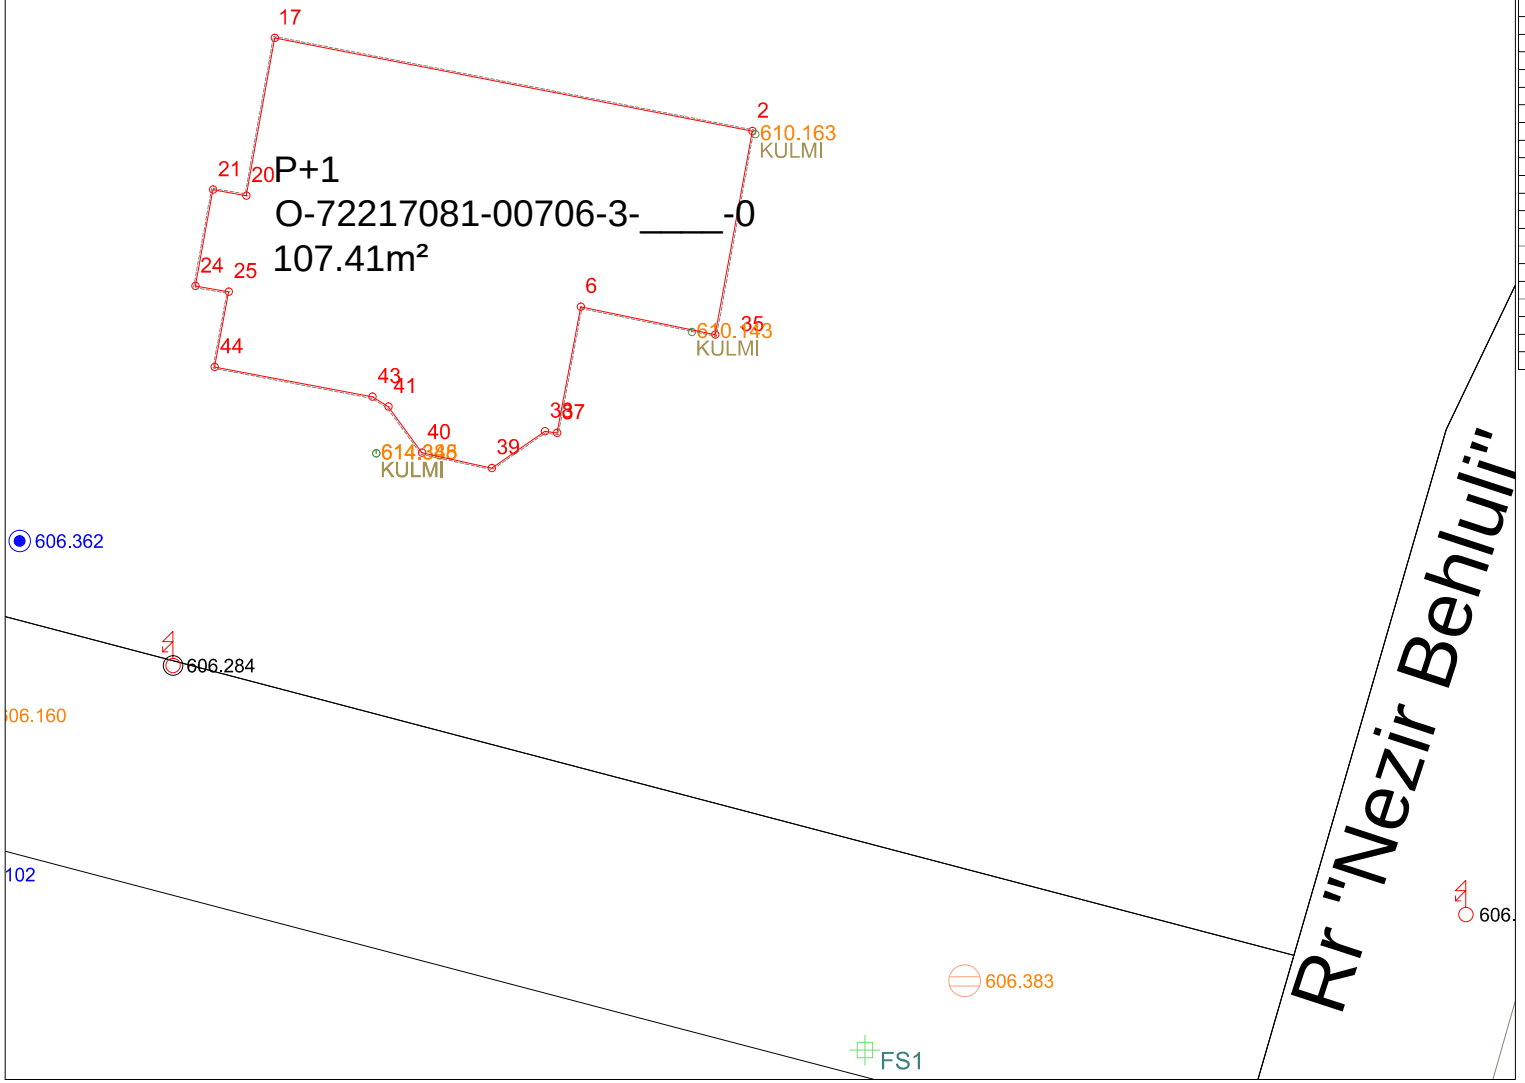

Republika e Kosovës

Qeveria -Vlada

Ministria e Mjedisit dhe Planifikimit Hapësinr /Ministarstv Sredine i Prstrng Planiranja

AGJENCIA KADASTRALE E KOSOVËS/ KATASTARSKA AGENCIJA KOSOVA

Situacioni i terrenit

Zyra kadastrale kmunale / pštinska katastarska kancelarija: Ferizaj

Zona kadastrale / Katastarska zona: Slivovë

Nr. i njësisë kadastrale / Br. katastarske jedinice : 706-3

Numri i lëndës / Broj predmeta: _____

Shkalla e zvoglimit / Razmera plana 1: 200

Lista e koordinatave të pikave të matura:

Nr	Y	X	H	DSC
319	7508342.699	4696784.165	606.735	BUNAR
310	7508344.823	4696753.620	606.392	FS1
311	7508313.671	4696747.366	605.763	FS2
15	7508331.896	4696769.398	614.388	KULMI
16	7508341.921	4696777.843	610.163	KULMI
47	7508331.897	4696769.402	614.345	KULMI
48	7508340.241	4696772.611	610.143	KULMI
312	7508281.679	4696775.746	605.981	P1
313	7508281.679	4696775.746	605.981	P1
314	7508354.808	4696749.871	607.437	P2
315	7508354.808	4696749.871	607.437	P2
316	7508367.412	4696756.371	607.215	P3
317	7508367.412	4696756.371	607.215	P3
318	7508342.989	4696783.814	606.735	P4
2	7508341.840	4696777.923	606.713	PERDHESA
6	7508337.302	4696773.278	606.713	PERDHESA
17	7508329.215	4696780.387	606.713	PERDHESA
20	7508328.464	4696776.214	606.713	PERDHESA
21	7508327.58	4696776.37	606.713	PERDHESA
24	7508327.11	4696773.82	606.713	PERDHESA
25	7508328	4696773.67	606.713	PERDHESA

Nr	Y	X	H	DSC
35	7508340.865	4696772.544	606.713	PERDHESA
37	7508336.678	4696769.938	606.713	PERDHESA
38	7508336.362	4696769.982	606.713	PERDHESA
39	7508334.951	4696769.015	606.713	PERDHESA
40	7508333.108	4696769.414	606.713	PERDHESA
41	7508332.215	4696770.638	606.713	PERDHESA
43	7508331.794	4696770.895	606.713	PERDHESA
44	7508327.626	4696771.688	606.713	PERDHESA
52	7508279.855	4696772.393	605.657	PUSET-F
59	7508321.341	4696762.470	606.160	PUSET-F
183	7508326.910	4696783.942	605.737	PUSET-F
234	7508330.299	4696817.440	605.632	PUSET-F
241	7508321.277	4696820.681	605.480	PUSET-F
302	7508347.459	4696755.447	606.383	PUSET-F
309	7508320.663	4696758.260	605.102	PUSET-U
324	7508322.462	4696767.082	606.362	PUSET-U
56	7508289.457	4696773.423	605.713	SHTYLL-EL
65	7508326.520	4696763.787	606.284	SHTYLL-EL
89	7508356.025	4696746.112	607.295	SHTYLL-EL
93	7508360.710	4696757.200	606.998	SHTYLL-EL

Shpjegues:

- Kufiri kadastral (nga SIKTK-G)
- Ndërtesa në trajtim për legalizim
- Ndërtesa tjera
- Aneks Ndërtimi
- Shtyllë elektrike
- Pusetë e ujësjellësit
- Pusetë e ujërave të zeza
- Strehët
- Kyqje në rrymë
- Pikë e objekteve fqinje
- Rr. Emri i rrugës
- P4 Pikë e rrjetës gjeodezike
- 131 Pikë e strehëve
- Pikë e terasës
- 10 Pikë e objektit
- Pikë e murit
- 92 Pikë e kulmit

Rilevoi / Snimi: LIRIDON SEJDIU

(emri dhe mbiemri i gjedetit/kompanisë/ ime i prezime gedeta/ kompanije)

Nr. i licencës / Br. licence: 140

Data e rilevimit / Datum snimanja: 18.11.2023

Nënshkrimi / Potpis: _____

V.V.